

1 PLANTA DE SITUAÇÃO
ESCALA 1/100


QUADRO DE ÁREAS (LOTE 207)	
Nº DE PAVIMENTOS	01
Á. DO TERRENO	236,17m ²
Á. TOTAL CONSTRUIDA	159,81m ²
Á. OCUPADA	159,81m ²
Á. PERMEÁVEL	57,37m ²
Á. DA PISCINA	10,00m ²
I.O.	0,67
I.U.	0,67
I.P.	0,24

(75) 98235-0660 |
Email: arq.urbfabio@hotmail.com

PROJETO RESIDENCIAL	
PROPRIETÁRIO	_____
ENDEREÇO	FEIRA DE SANTANA - BA
PROJETO	PLANTA DE LOCALIZAÇÃO
FASE	PROJETO EXECUTIVO
ARQUITETA	Fabio Rebouças
FOLHA	
01	
ESCALA	1/75
DATA	ABR/25

LEGENDA

- 01 RETIRAR ESQUADRIA EXISTENTE E DEMOLIR PAREDE ATÉ O TETO.
- 02 FECHAR ABERTURA EXISTENTE.
- 03 RETIRAR OU MODIFICAR BANCADA EXISTENTE E FAZER AS ADAPTAÇÕES.
- 04 RETIRAR ESQUADRIA EXISTENTE, AUMENTAR ABERTURA , COLOCAR BANCADA NOVA E MODIFICAR PONTO DE SAÍDE DE GÁS..
- 05 ASSENTAR ESQUADRIA RETIRADA DO PONTO 01.
- 06 AUMENTAR BANHEIRO E MODIFICAR O LAYOUT.
- 07 RETIRAR PAREDE E AMPLIAR AMBIENTE.
- 08 RETIRAR PAREDE E AMPLIAR AMBIENTE.
- 09 ISOLAR PONTO HIDRÁULICO.
- 10 CONSTRUIR PISCINA (PROFOUNDIDADE A DEFINIR).
- 11 PILAR INTEGRADO AO BALCÃO.
- DEMOLIR
- CONSTRUIR

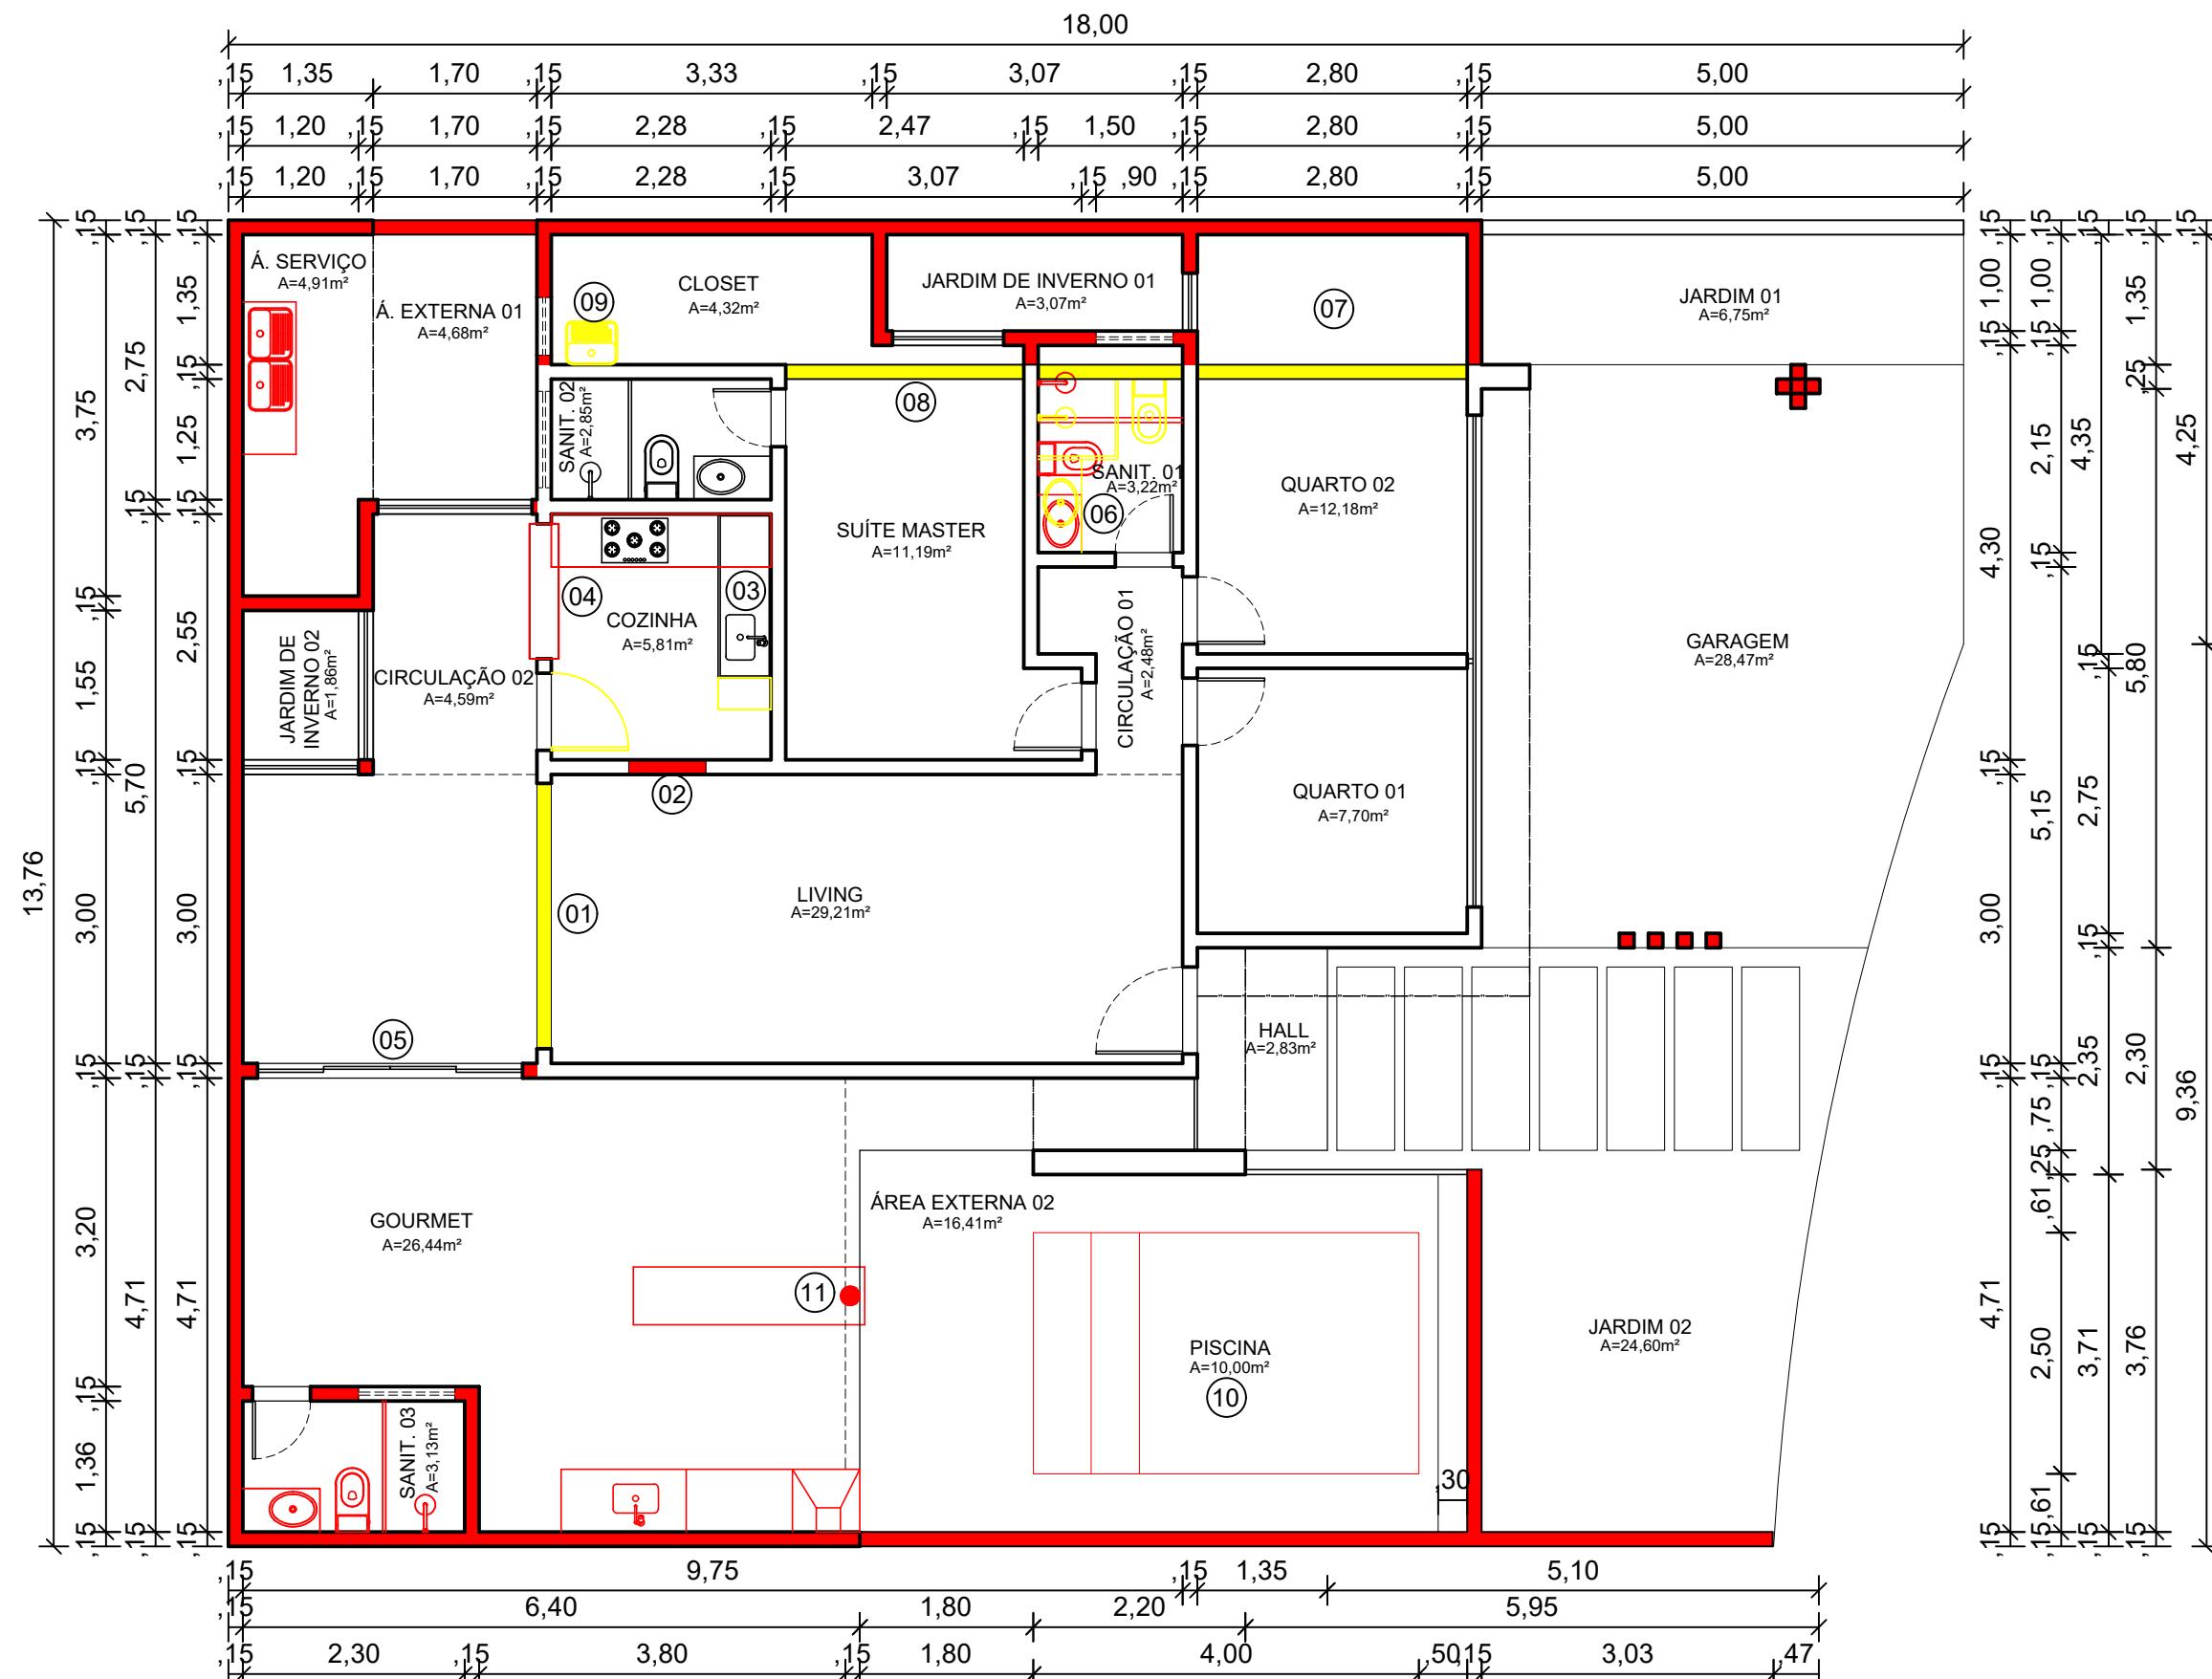

1 PLANTA DE REFORMA
ESCALA 1/75

(75) 98235-0660 |
Email: arq.urbfabio@hotmail.com


PROJETO RESIDENCIAL	
PROPRIETÁRIO	_____
ENDEREÇO	FEIRA DE SANTANA - BA
PROJETO	DEMOLIR-CONSTRUIR
FASE	PROJETO EXECUTIVO
ARQUITETA	Fabio Rebouças

FOLHA 02

ESCALA 1/75
DATA ABR/25

TABELA DE ESQUADRIAS

SÍMBOLO	DIMENSÃO	TIPO	MATERIAL
P1	0,90X2,50	ABRIR	PVC
P2	0,70X2,10	ABRIR	PVC
P3	0,60X2,10	ABRIR	PVC
P4	2,75X2,10	CORRER 4 FOLHAS	PVC+VIDRO
P5	1,60X2,10	CORRER 2 FOLHAS	PVC+VIDRO
P6	0,75X2,50 0,75X1,95	ABRIR FIXA	ALUMÍNIO +VIDRO
J1	1,20X1,50 H=0,50	CORRER	PVC+VIDRO
J2	1,55X1,50 H=0,50	CORRER	PVC+VIDRO
J3	2,47X2,00 H=0,60	CORRER	PVC+VIDRO
J4	0,60X2,00 H=0,60	ABRIR	PVC+VIDRO
J5	1,20X1,10 H=1,00	CORRER	PVC+VIDRO
J6	0,60X0,50 H=1,70	BASCULAR	PVC+VIDRO
J7	1,00X0,50 H=1,70	BASCULAR	PVC+VIDRO
J8	0,80X0,50 H=1,70	BASCULAR	PVC+VIDRO
GRADE	2,30X2,60	FIXA	ALUMÍNIO +VIDRO

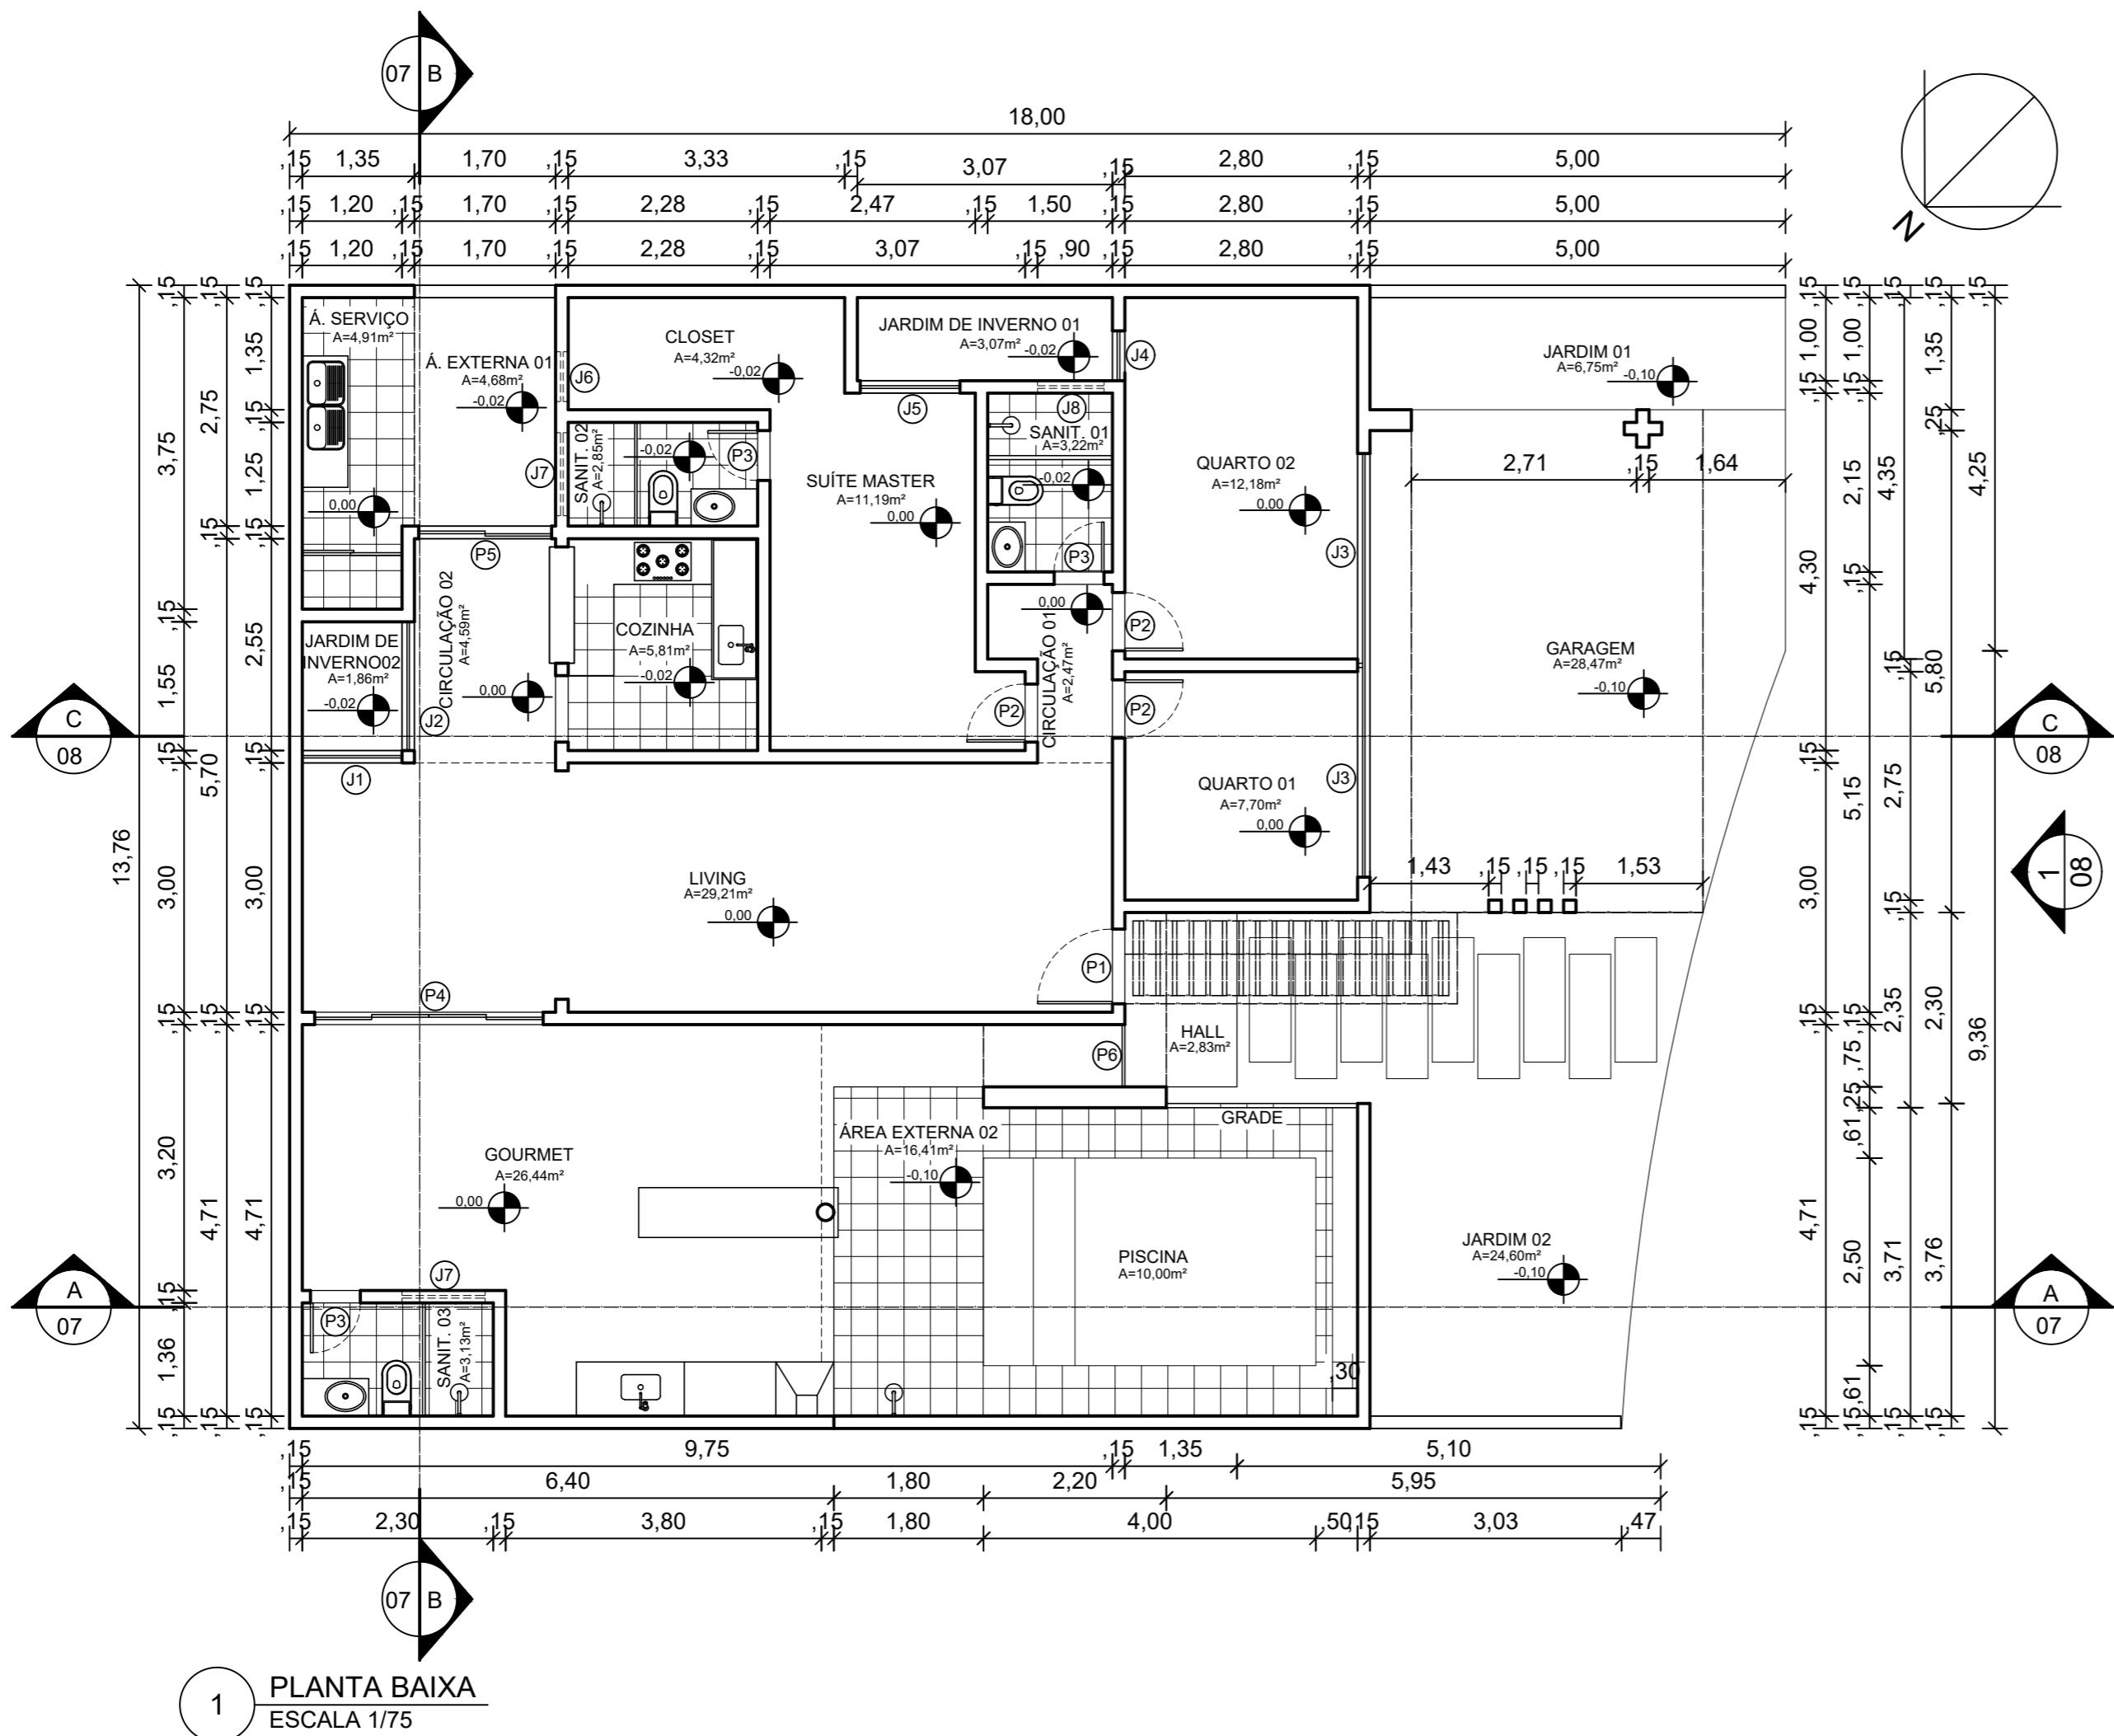


(75) 98235-0660 |
Email: arq.urbfabio@hotmail.com

PROJETO RESIDENCIAL

PROPRIETÁRIO _____
ENDEREÇO FEIRA DE SANTANA - BA
PROJETO PLANTA BAIXA
FASE PROJETO EXECUTIVO
ARQUITETA Fabio Rebuças

03

ESCALA 1/75
DATA ABR/25

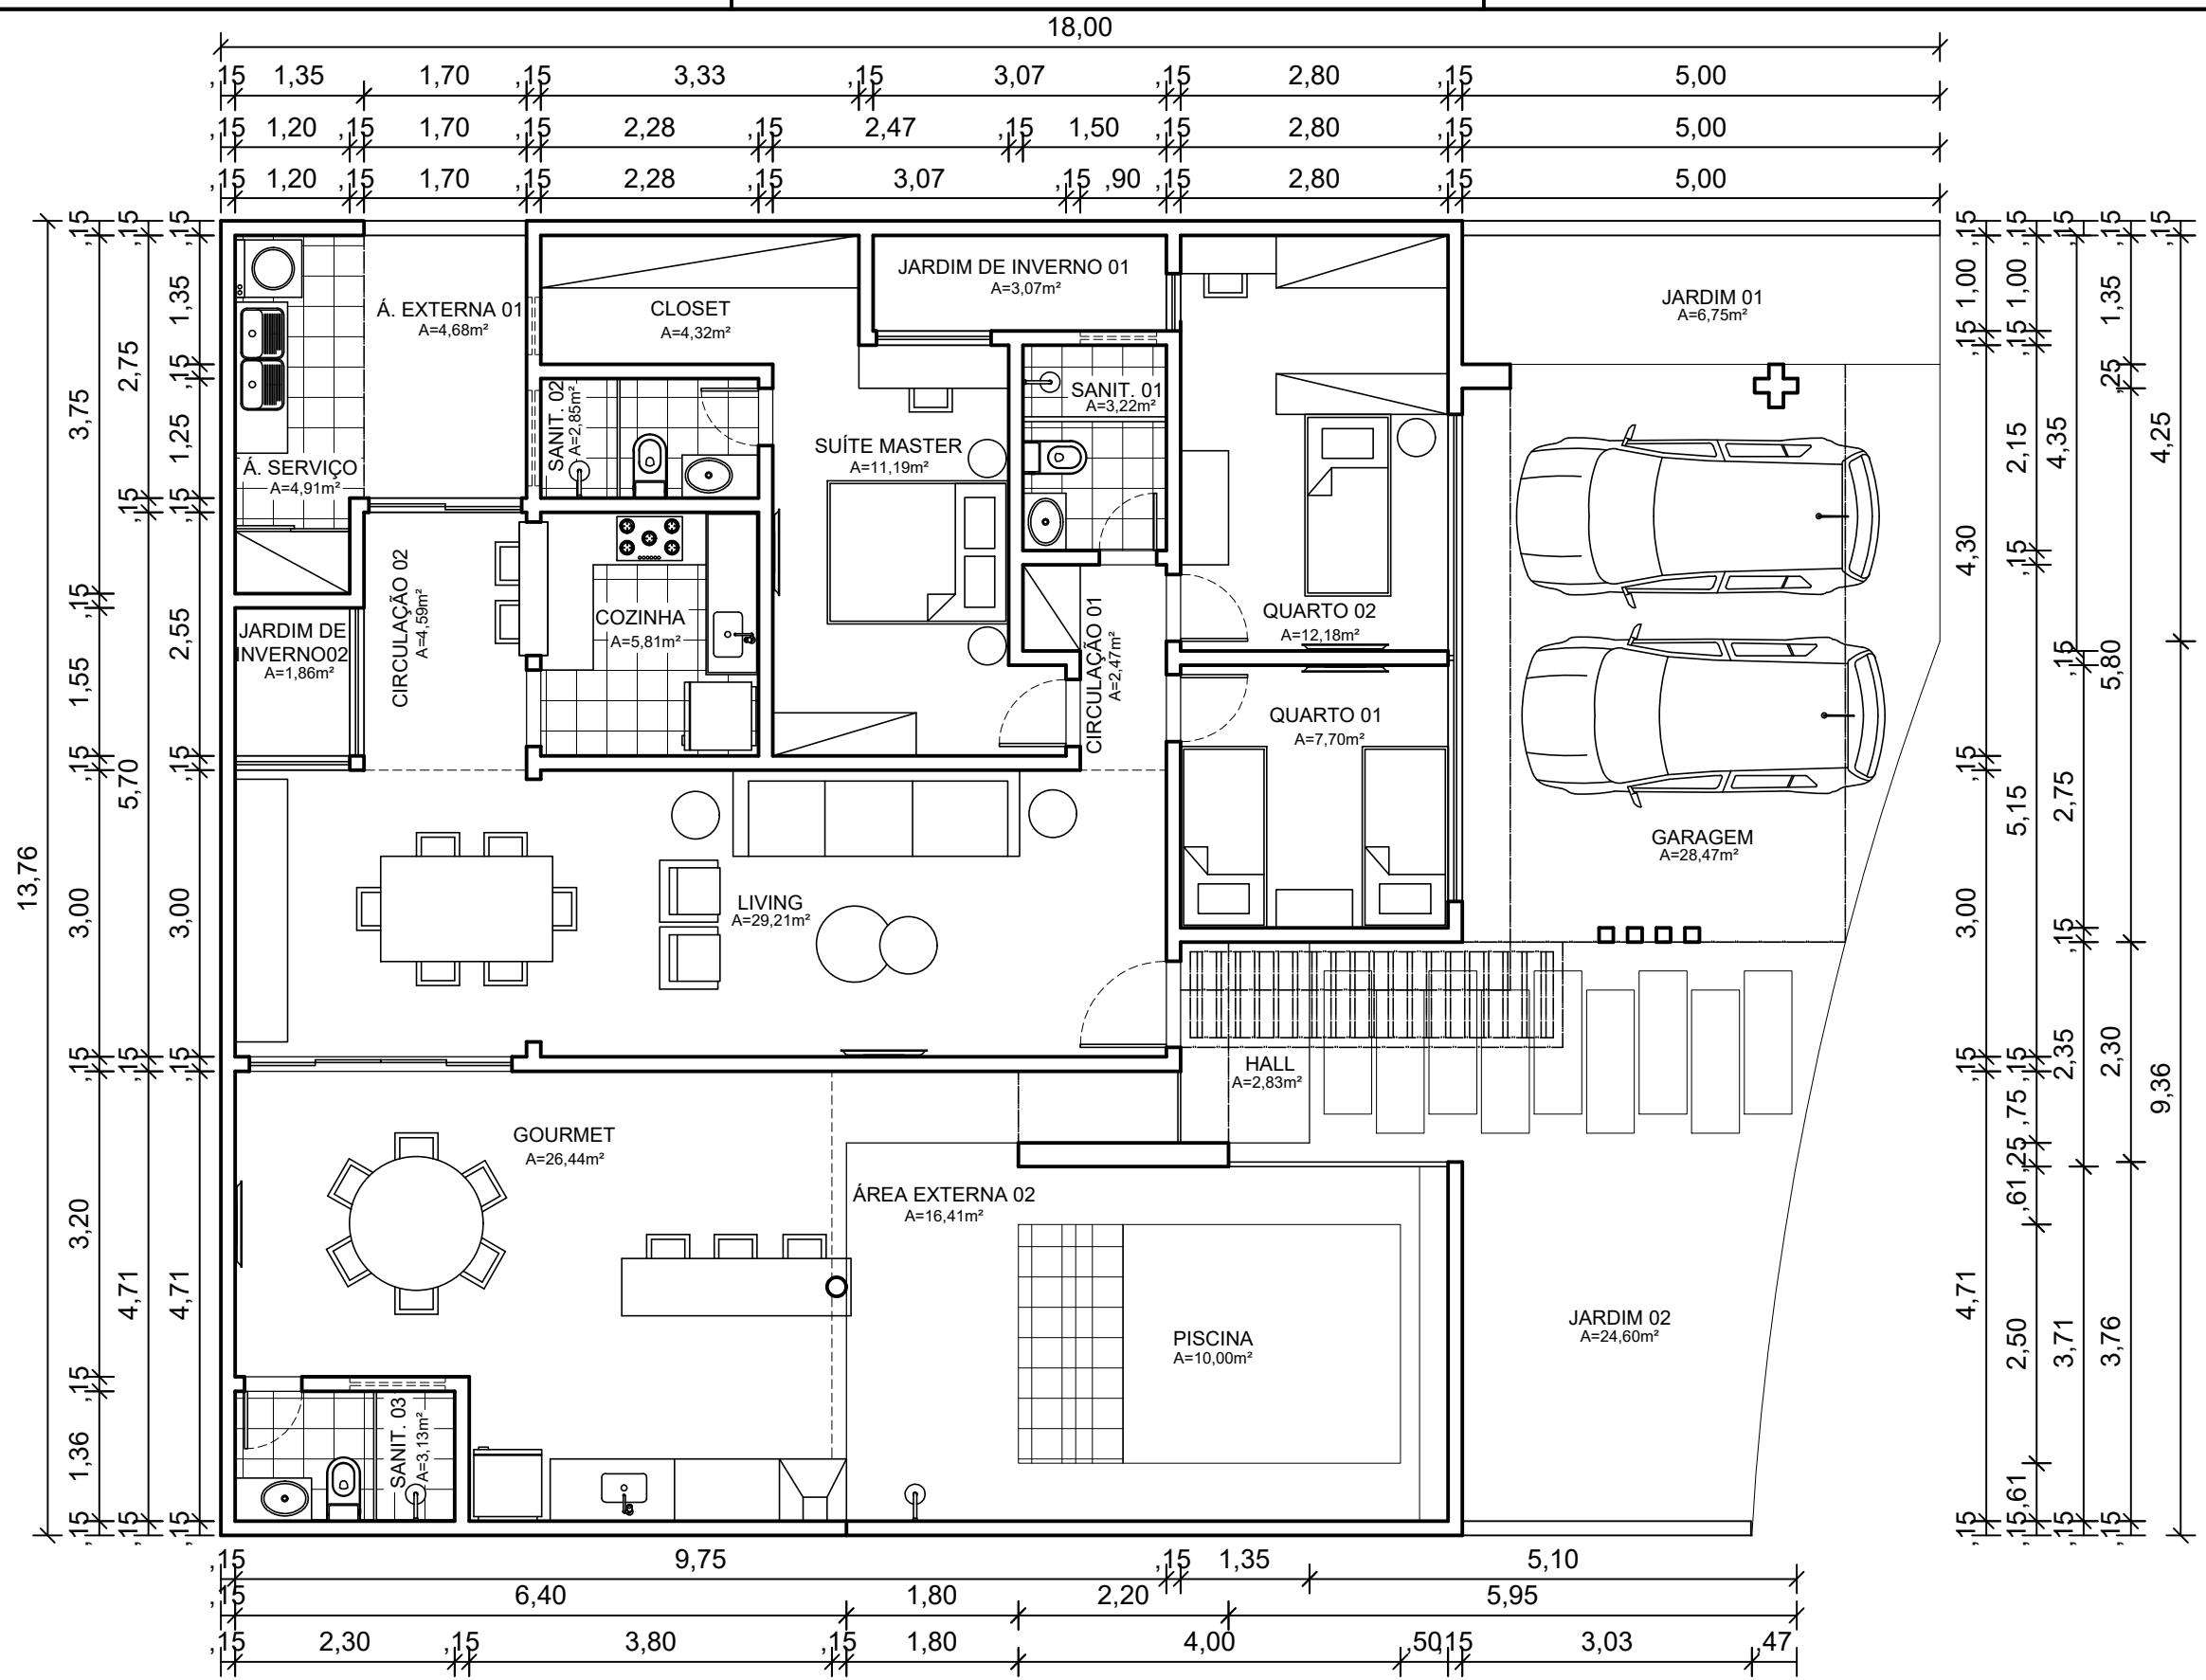

1

PLANTA DE LAYOUT
ESCALA 1/75

(75) 98235-0660 |
Email: arq.urbfabio@hotmail.com

FOLHA


04

PROJETO RESIDENCIAL


PROPRIETÁRIO _____
ENDEREÇO FEIRA DE SANTANA - BA
PROJETO PLANTA DE LAYOUT
FASE PROJETO EXECUTIVO
ARQUITETA Fabio Rebouças

ESCALA 1/75

DATA ABR/25

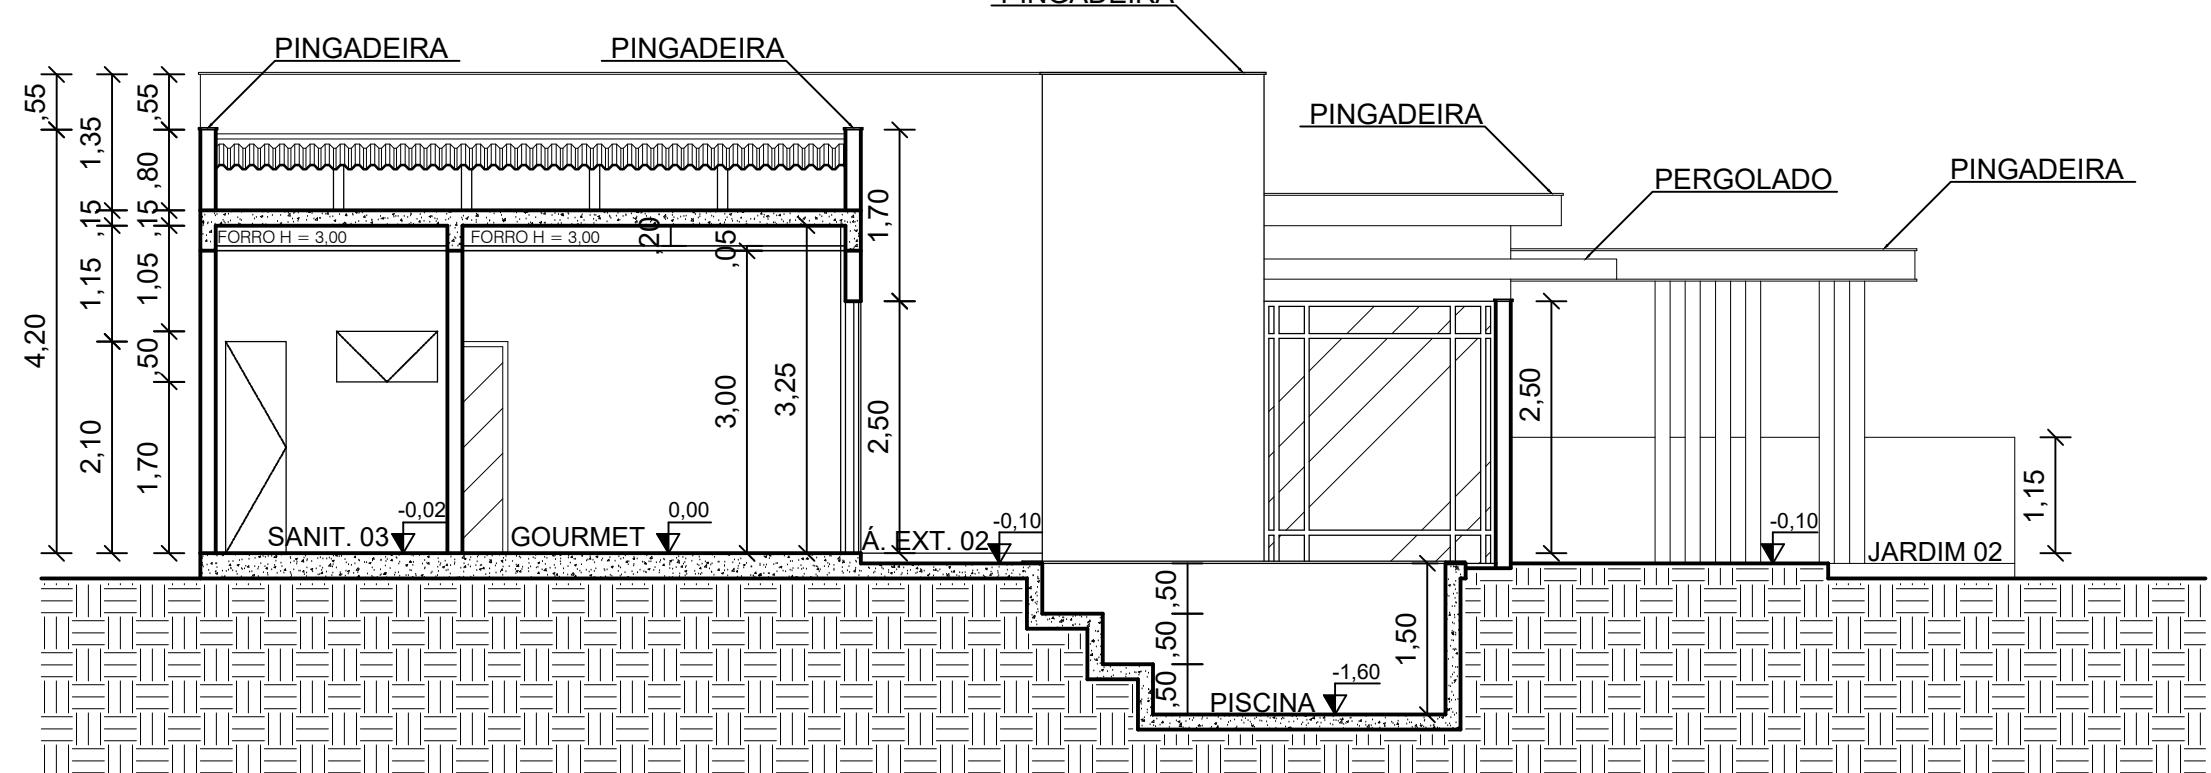

1 CORTE AA
ESCALA 1/75

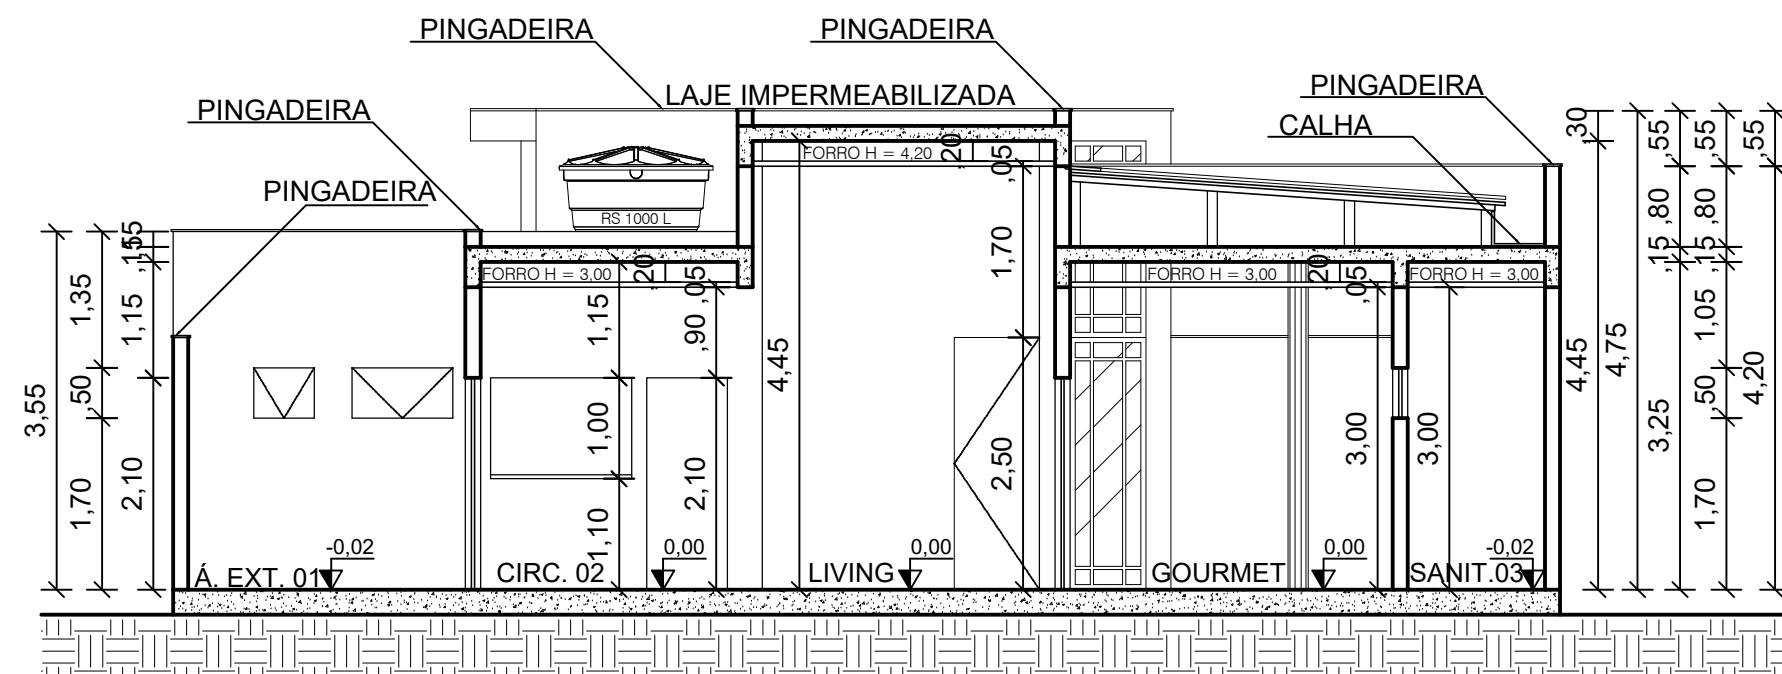

2 CORTE BB
ESCALA 1/75


(75) 98235-0660 |
Email: arq.urbfabio@hotmail.com

PROJETO RESIDENCIAL	
PROPRIETÁRIO	_____
ENDEREÇO	FEIRA DE SANTANA - BA
PROJETO	CORTES
FASE	PROJETO EXECUTIVO
ARQUITETA	Fabio Rebouças


FOLHA **05**

ESCALA 1/75

DATA ABR/25

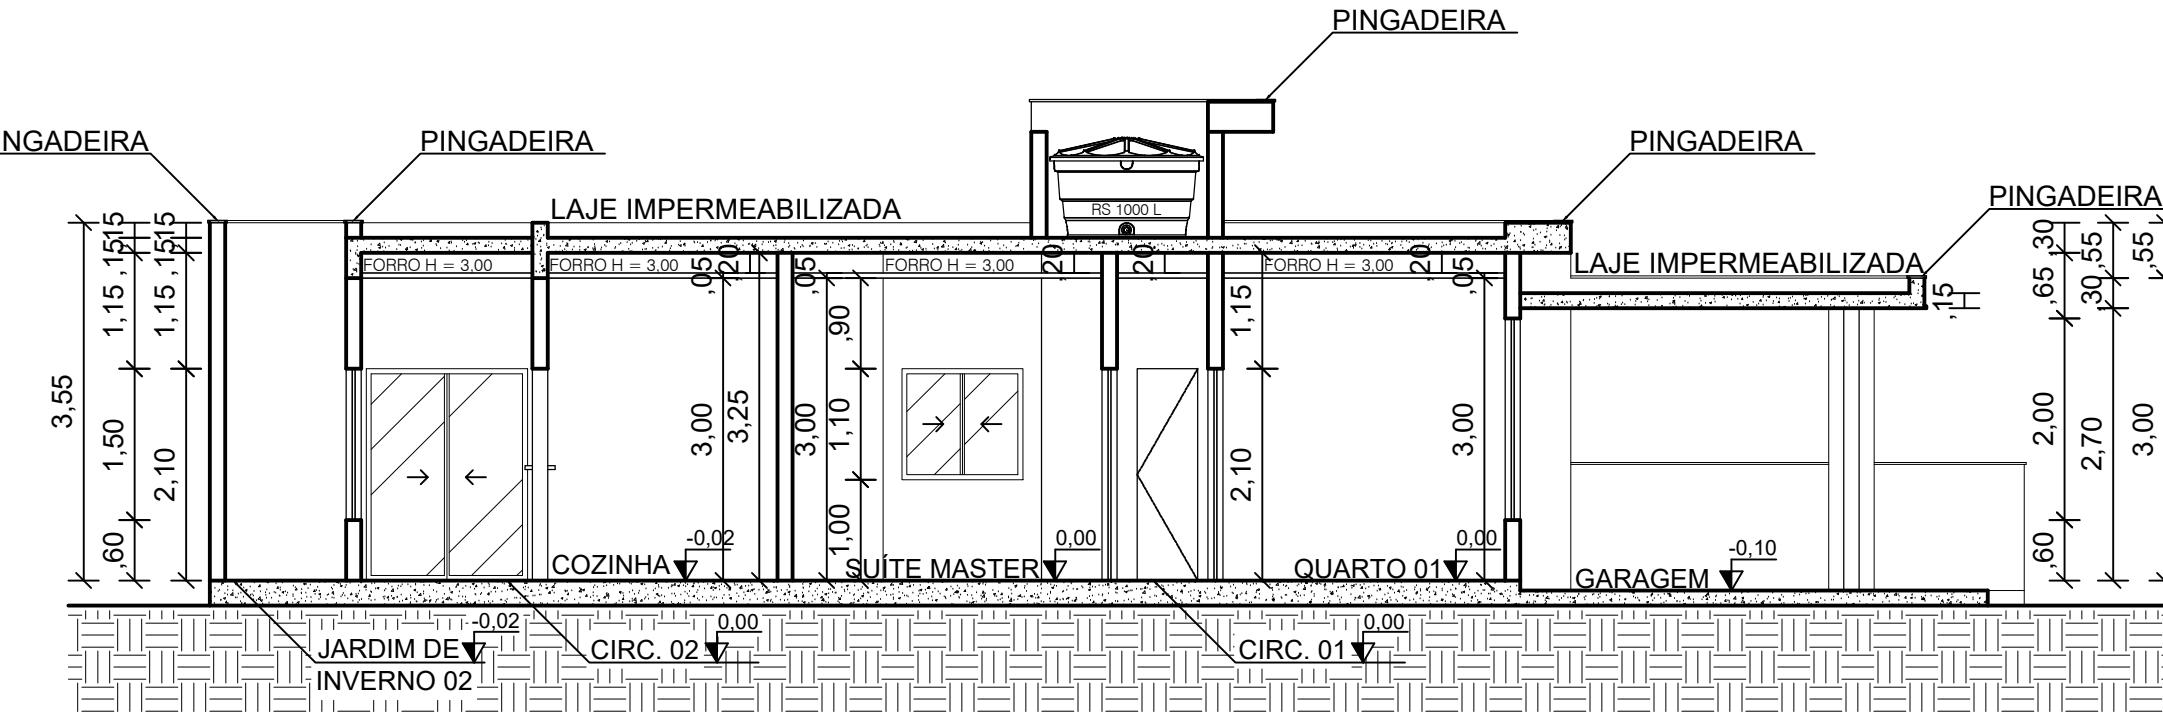

1 CORTE CC
ESCALA 1/75

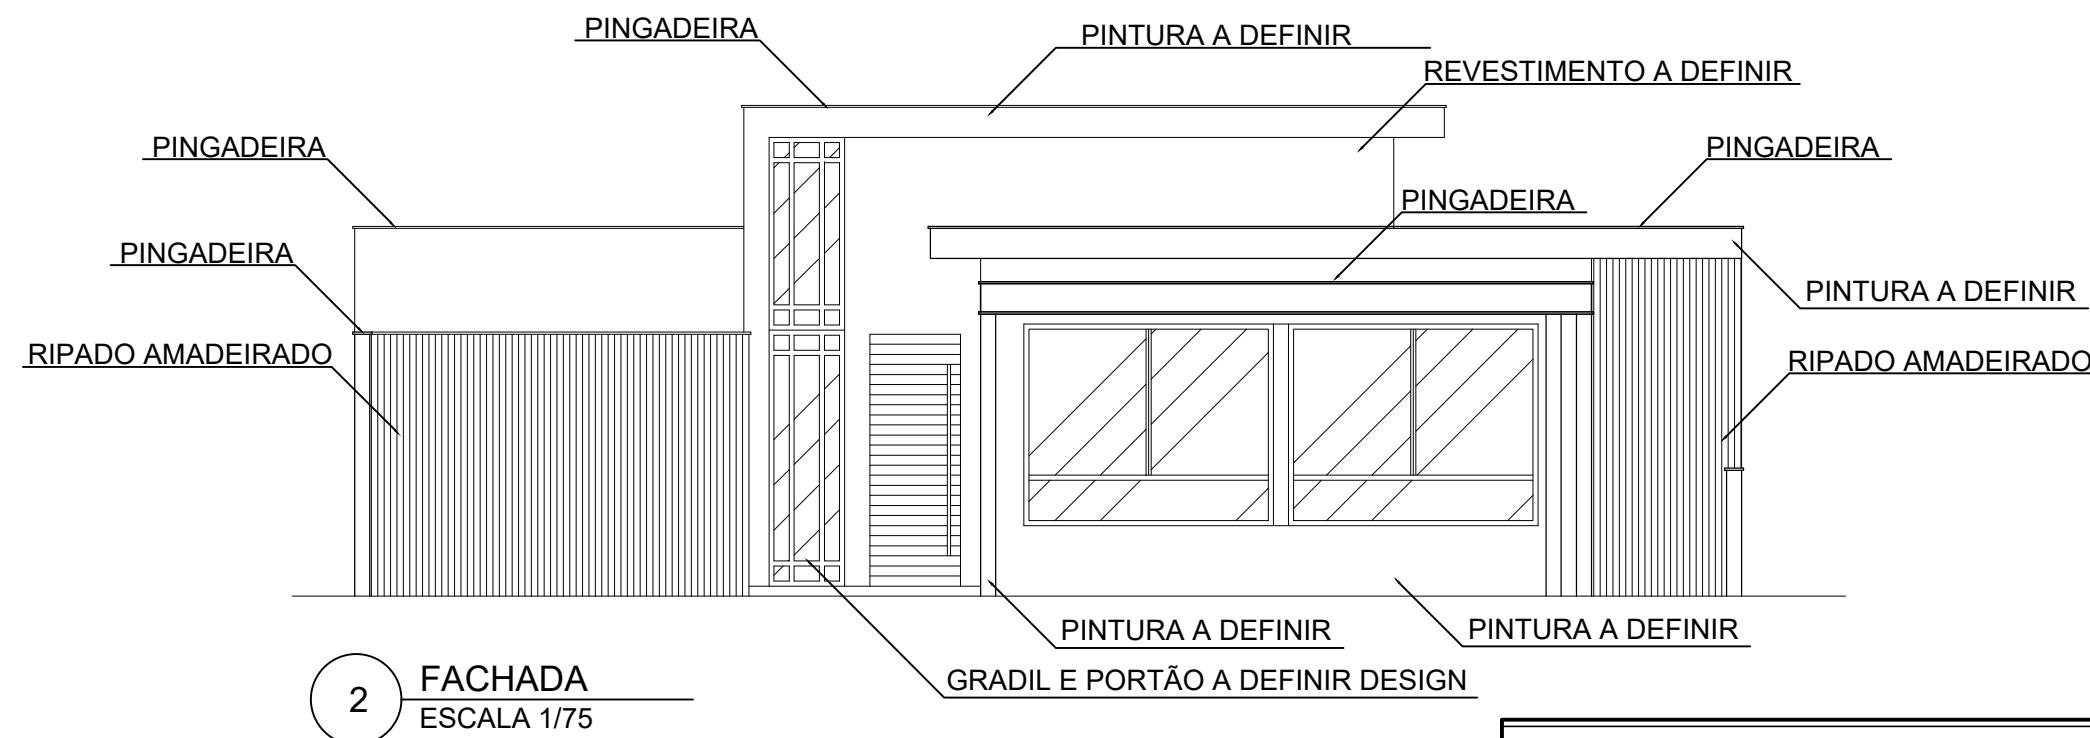

2 FACHADA
ESCALA 1/75

(75) 98235-0660 |
Email: arq.urbfabio@hotmail.com


PROPRIETÁRIO	
ENDEREÇO	FEIRA DE SANTANA - BA
PROJETO	CORTE-FACHADA
FASE	PROJETO EXECUTIVO
ARQUITETA	Fabio Rebouças

FOLHA


06

ESCALA 1/75

ADR/23

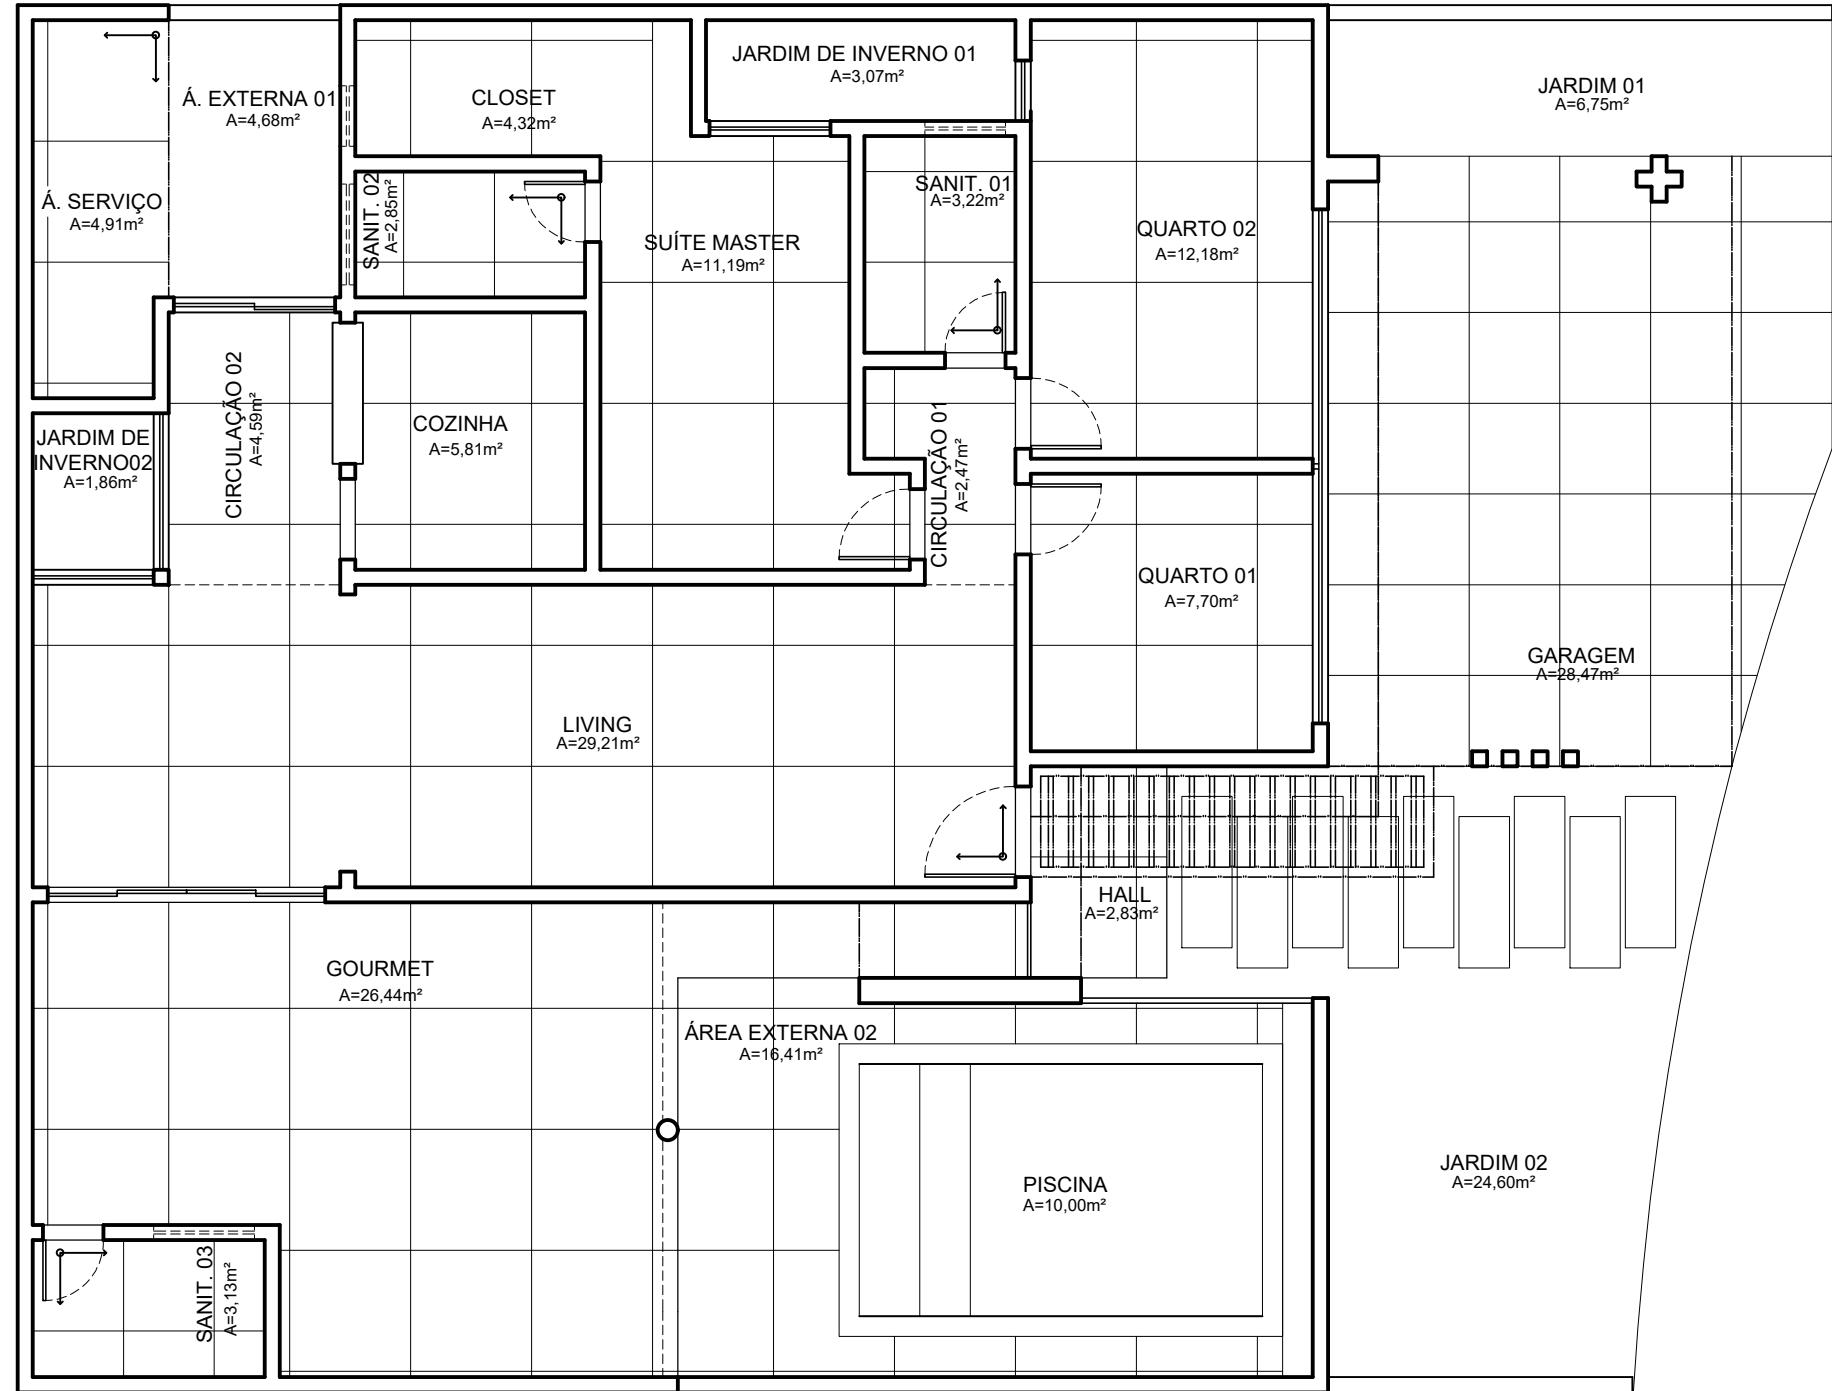

1 PLANTA DE PAGINAÇÃO DE PISO
ESCALA 1/75

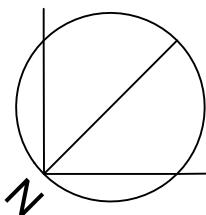


OBS: A PAGINAÇÃO DE PISO DEFINITIVA SERÁ FEITA APÓS A ESCOLHA DOS PISOS.
A PAGINAÇÃO DE REVESTIMENTOS SERÁ FEITA APÓS A ESCOLHA DOS REVESTIMENTOS.

(75) 98235-0660 |
Email: arq.urbfabio@hotmail.com

PROJETO RESIDENCIAL
PROPRIETÁRIO _____
ENDEREÇO FEIRA DE SANTANA - BA
PROJETO PAGINAÇÃO DE PISO
FASE PROJETO EXECUTIVO
ARQUITETA Fabio Rebouças


07

ESCALA 1/75
DATA ABR/25

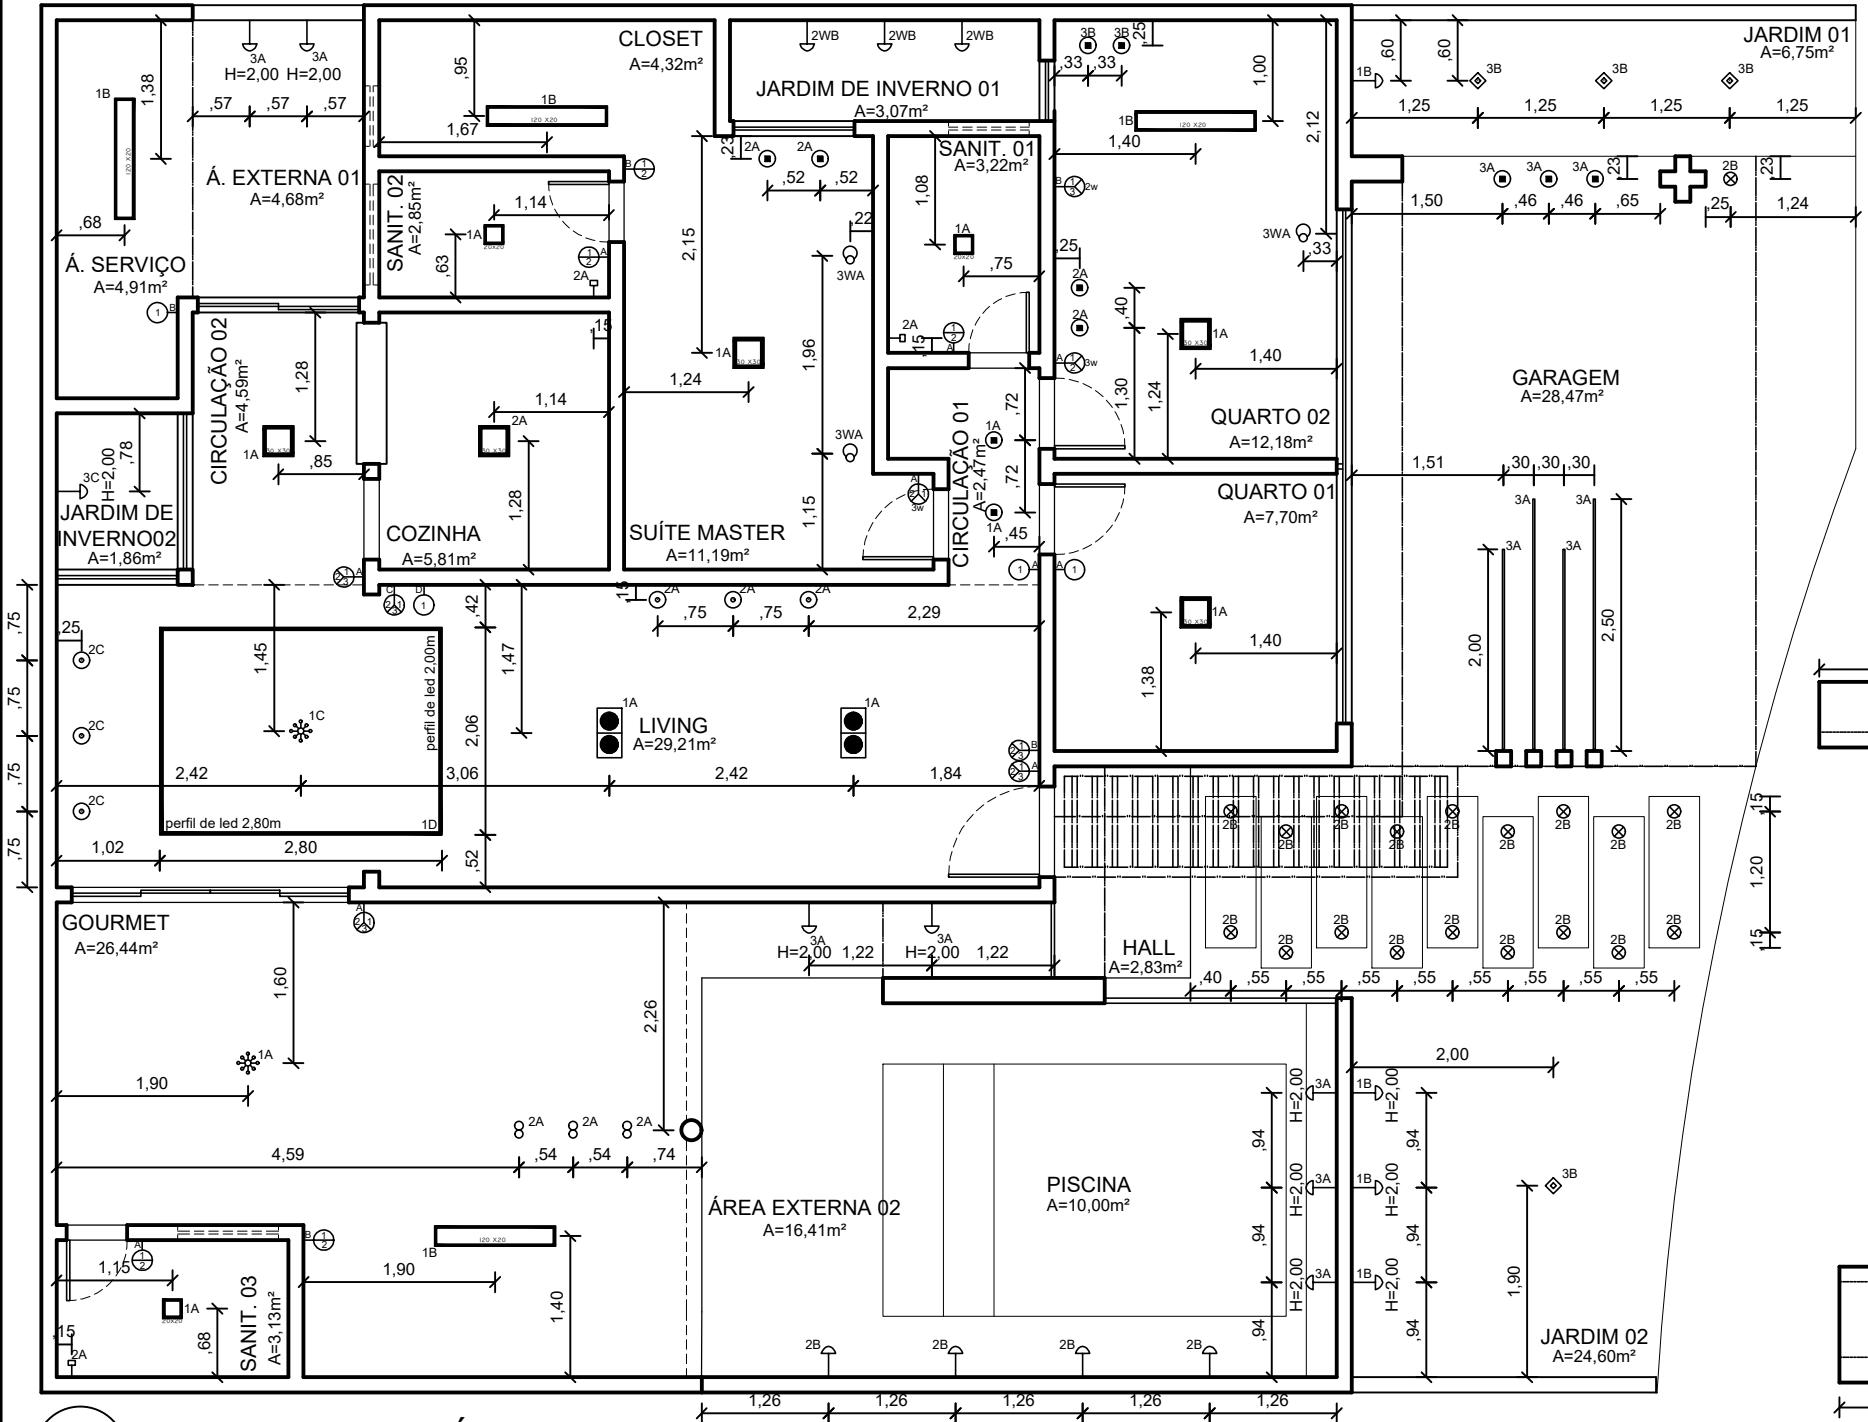


1 PLANTA LUMINOTÉCNICA
ESCALA 1/75


SÍMBOLO	TIPO	TEMPERATURA	IRC	LUMENS	SÍMBOLO	TIPO	TEMPERATURA	IRC	LUMENS
○	DICROICA AR111	3000K	>80	500	⊗	BALIZADOR DE PISO	3000K	>80	150
■	DICROICA	3000K	>80	500	◊	ESPETO DE JARDIM	3000K	>80	350
—	PERFIL DE LED 1	3000K	>80	1200 - 1500	* ¹	PENDENTE 1	4000K	>80	1950
—	PERFIL DE LED 2	3000K	>80	1350	8	PENDENTE 2	3000K	>80	350
[]	PLAFON 120X20	4000K	>80	1700 - 2000	♀	PENDENTE 3	3000K	>80	500
●●	MIX 2 LAMP.	3000K	>80	1950	↓	ARANDELA	3000K	>80	500
□	PLAFON 30X30	4000K	>80	1200-1500	↑	ILUMINAÇÃO NO ESPELHO	4000K	>80	SEGUIRÁ ESPECIFICAÇÃO DO TAMANHO DO ESPELHO
□	PLAFON 20X20	4000K	>80	1000 - 1200					

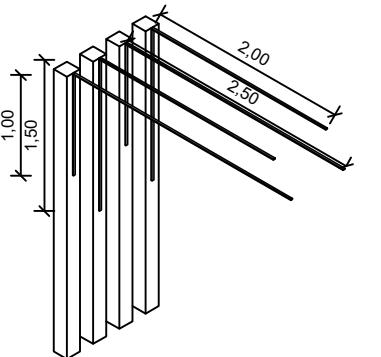

2 ILUMINAÇÃO PILARES GARAGEM
ESCALA 1/75

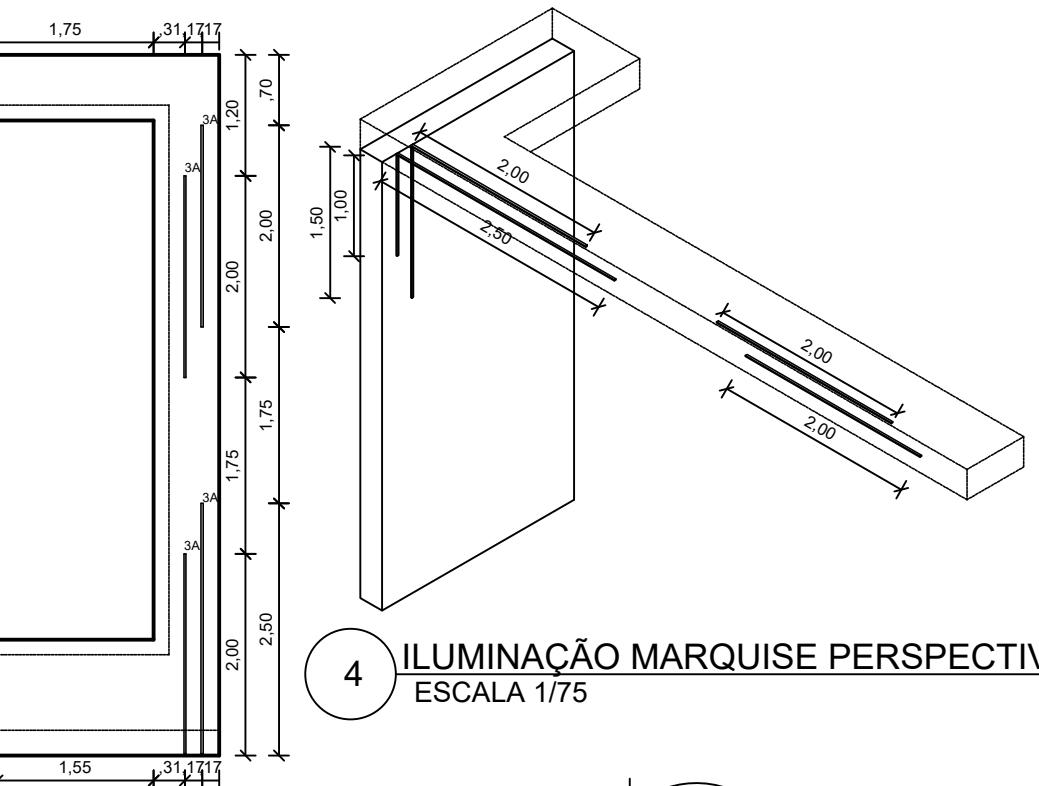

3 ILUMINAÇÃO MARQUISE
ESCALA 1/75

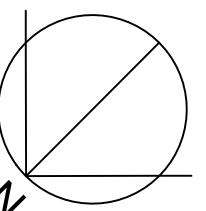



(75) 98235-0660 |
Email: arq.urbfabio@hotmail.com

FOLHA
08

PROJETO RESIDENCIAL

PROPRIETÁRIO _____
ENDERÉCOS FEIRA DE SANTANA - BA
PROJETO LUMINOTÉCNICO
FASE PROJETO EXECUTIVO
ARQUITETA Fabio Rebouças

ESCALA 1/75
DATA ABR/25

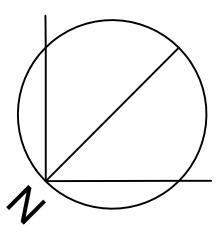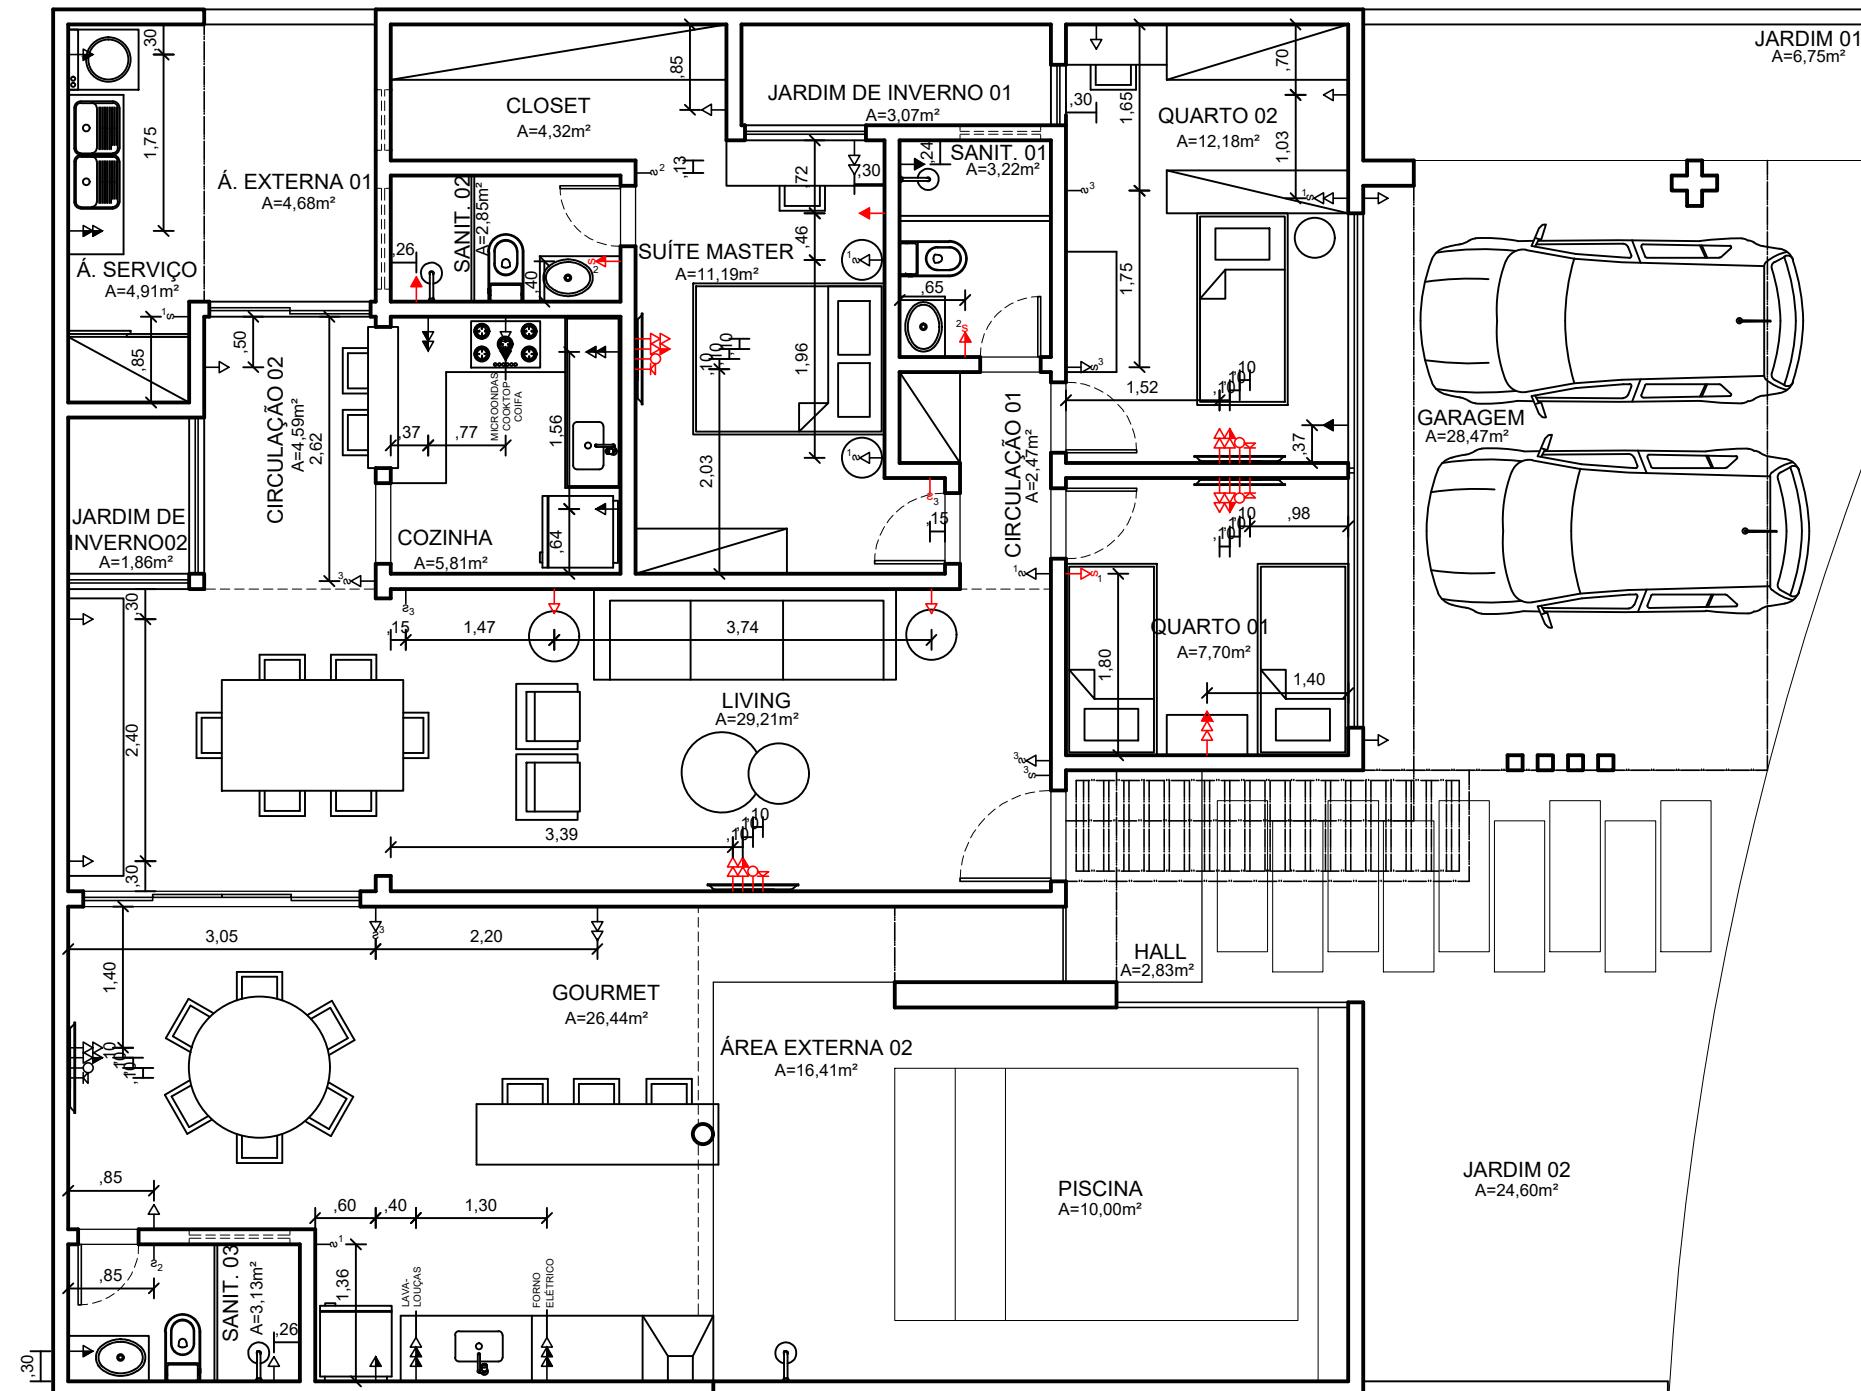



1 PLANTA DE PONTOS ELÉTRICOS
ESCALA 1/75

—○	INTERRUPTOR	h=1,30m
→	TOMADA BAIXA	h=0,40m
→	TOMADA MÉDIA	h=1,30m
→	TOMADA ALTA	h=2,20m
—○	ANTENA	h=1,30m
—	INTERNET	h=0,40m

● MANTER
● PONTO NOVO


(75) 98235-0660 |
Email: arq.urbfabio@hotmail.com

FOLHA	
09	
PROJETO RESIDENCIAL	
PROPRIETÁRIO	_____
ENDEREÇO	FEIRA DE SANTANA - BA
PROJETO	PLANTA DE PONTOS DE TOMADAS
FASE	PROJETO EXECUTIVO
ARQUITETA	Fabio Rebouças
ESCALA	1/75
DATA	ABR/25

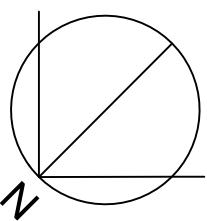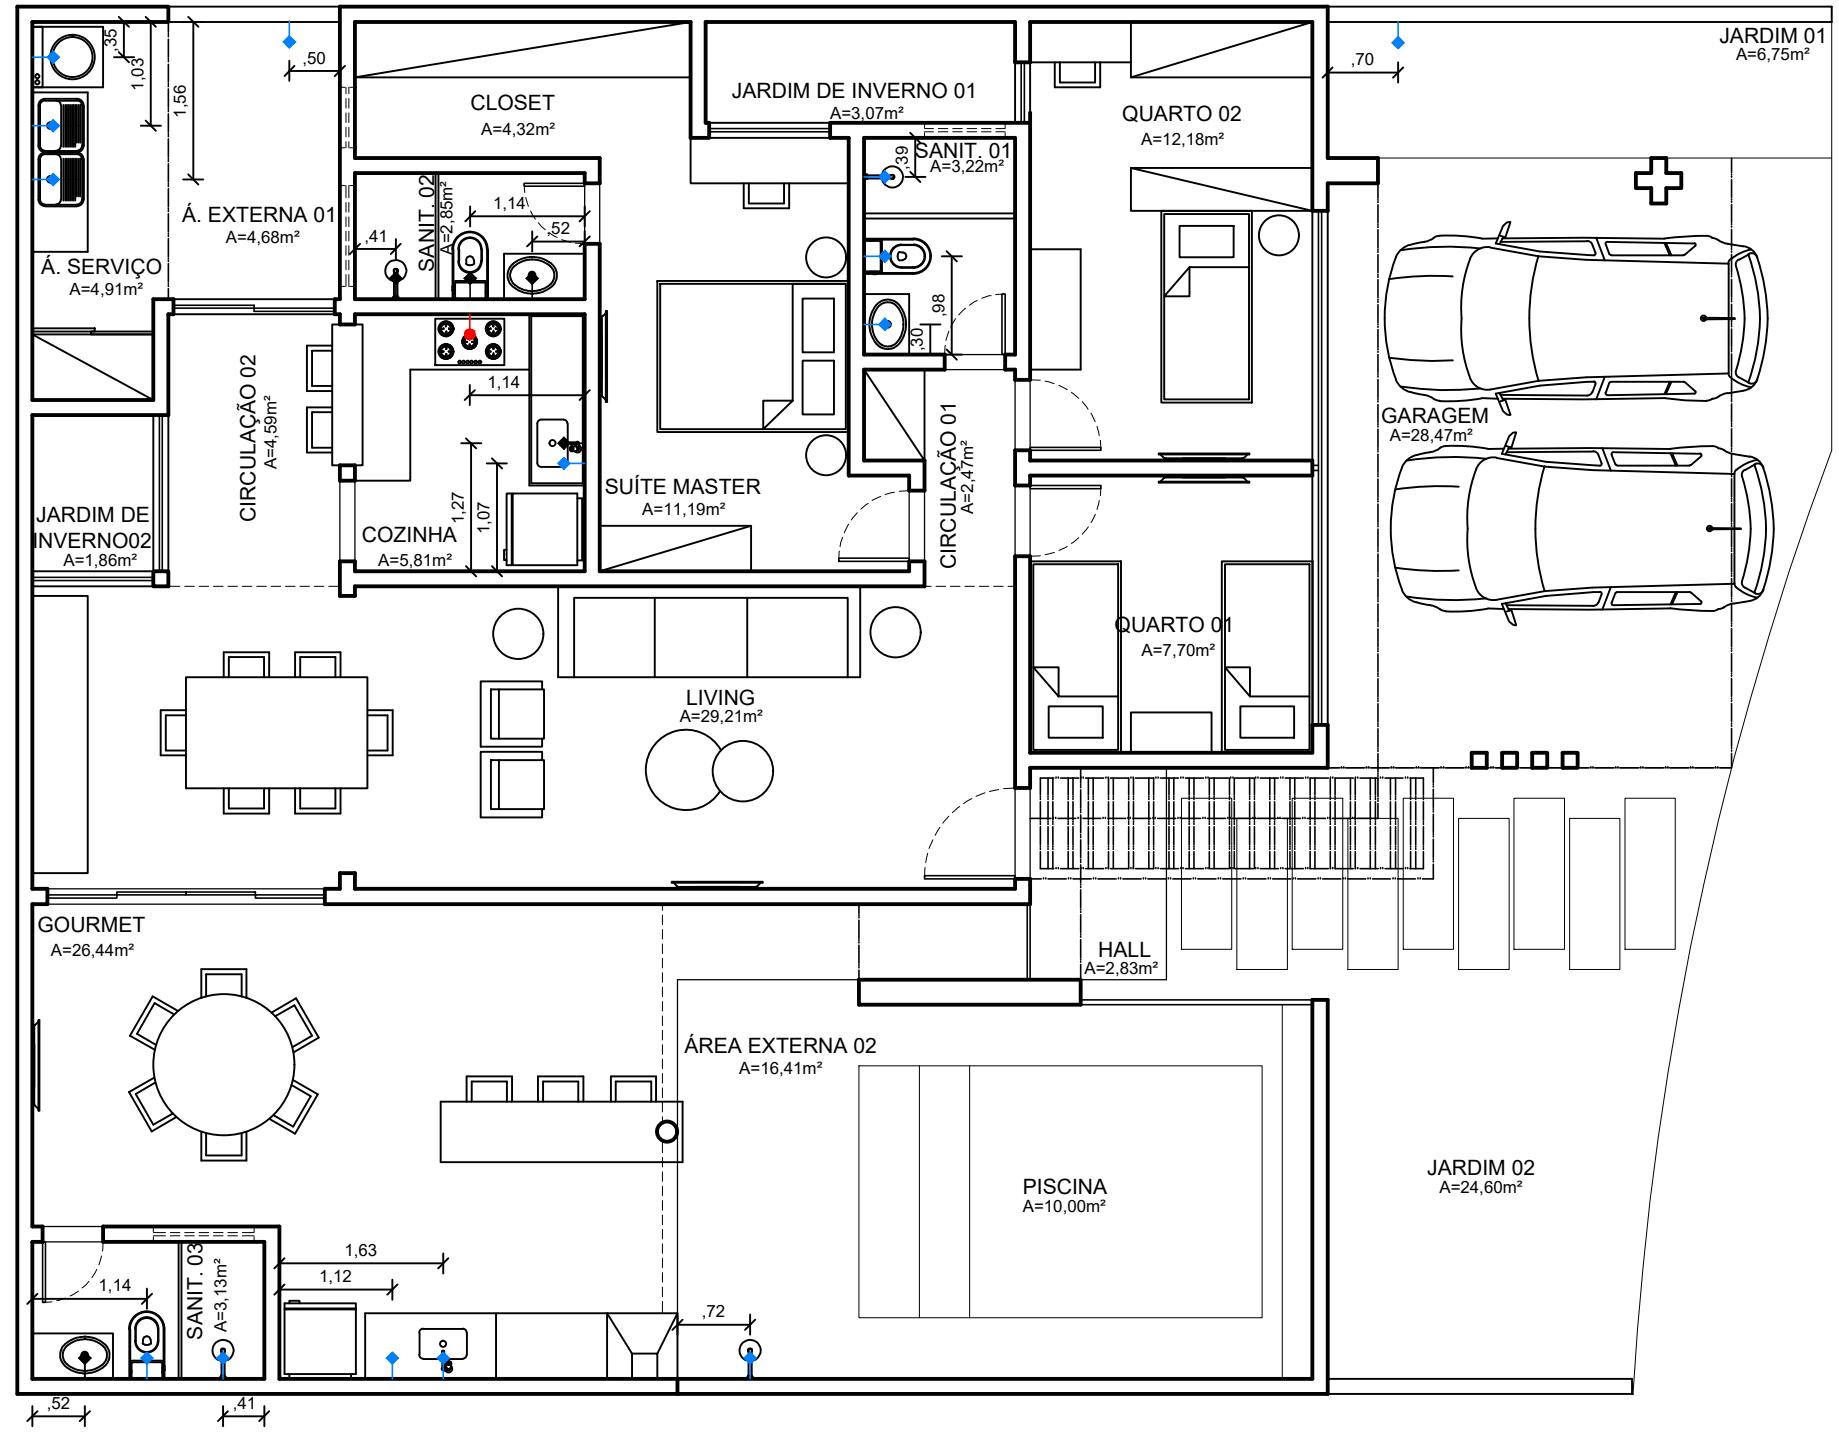

1) PLANTA DE PONTOS HIDRÁULICOS

ESCALA 1/75

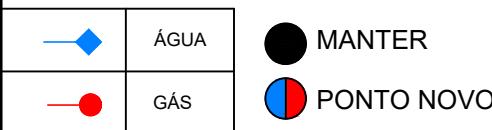

(75) 98235-0660 |
Email: arq.urbfabio@hotmail.com

PROPRIETÁRIO _____

ENDEREÇO FEIRA DE SANTANA - BA

PROJETO PLANTA DE PONTOS HIDRÁULICOS

FASE PROJETO EXECUTIVO

ARQUITETA Fabio Rebouças

PROJETO RESIDENCIAL

FOLHA

10

ESCALA 1/75
DATA ABR/25

